LABORATÓRIO COLABORATIVO: Dinâmicas Urbanas, Património, Artes
XI Seminário de Investigação, Ensino e Difusão

28 e 29 de agosto de 2025, Centro Histórico e Cultural do Mackenzie

CONVENTO DA TOMINA: CONTRIBUTOS PARA A COMPREENSÃO DA SUA IDENTIDADE PATRIMONIAL

CARLOTA ROCHA E PROF. SOFIA ALEIXO
Dep. Arquitetura – EAartes – Universidade de Évora

UNIVERSIDADE DE ÉVORA
iscte INSTITUTO UNIVERSITÁRIO DE LISBOA
Mackenzie
15 ANOS 1870-2025

CONVENTO DA TOMINA

Contribuir para a sua valorização e preservação.

Evitar a sua perda definitiva e reforçar a sua identidade patrimonial.

A Arquitetura garante a conexão com o passado.

Turgeon (2009)

Carta de Nara (UNESCO, ICCROM, ICOMOS) (1994)

Autenticidade Material e Imaterial

ÍNDICE

1. ENQUADRAMENTO E CONTEXTO

2. FUNDAÇÃO E CONSTRUÇÃO

3. ”ESPÍRITO DO LUGAR”

4. CONSIDERAÇÕES FINAIS

SUSTENTABILIDADE SOCIOCULTURAL DO PATRIMÓNIO

CONTEXTO EM QUE SE INSERE A HISTÓRIA DA SUA FORMAÇÃO

Lecoq, 2014
Caldeira, 2016
Jorge, séc. XVIII
Franco, Mourão, Gomes, 2001
Notícias do Convento da Tomina, 1987

COMPREENSÃO SOBRE O SIGNIFICADO DE `SUSTENTABILIDADE SOCIOCULTURAL`

Brunland, 1987
UNESCO, 2020
Pessoa, 2001
Ponte, 2016
Sousa, 2015
Tilden, 1977
Vieira, Lacerda, 2010

DIMENSÃO IMATERIAL E SIMBÓLICA

ICOMOS, 1994
Themudo-Barata,
Mascarenhas, Capelo, 2014
Norberg-Schulz, 1976
Turgeon, 2009
ICOMOS, 2008
Torrico, 1999
Morón, 2003

ANÁLISE ARQUITETÓNICA E MATERIAL

Caldeira, 2016
Jorge, séc. séc. XVIII
Bispo, 1758
Lecoq, 2014
Arcebisto de Evora, n.d

METODOLOGIA DE INVESTIGAÇÃO

REVISÃO BIBLIOGRÁFICA E ANÁLISE DOCUMENTAL

CASOS DE ESTUDO COMPARATIVOS

`OBSERVAÇÃO-PARTICIPANTE` NAS FESTAS

REGISTO FOTOGRÁFICO

LEVANTAMENTO IN LOCO

OBJETIVOS

EVITAR A PERDA DEFINITIVA DO CONVENTO

CRIAR BASES METODOLÓGICAS APLICÁVEIS A OUTROS CASOS SEMELHANTES

CONTRIBUIR PARA A VALORIZAÇÃO CULTURAL E IDENTITÁRIA DE SANTO ALEIXO

REFUNCIONALIZAR O PATRIMÓNIO

PROPOSTA DE SALVAGUARDA E VALORIZAÇÃO DO CONVENTO DA TOMINA

Convento localizado nos limites da Herdade da Contenda

Perímetro Florestal da Contenda

1. ENQUADRAMENTO E CONTEXTO

Convento da Tomina - séc. XVII (1686).

Herdade da Contenda - Santo Aleixo da Restauração - Baixo Alentejo (região sul de Portugal).

Proteção apenas se encontra salvaguardada pelo *Plano Sectorial da Rede Natura 2000*, como "Sítio de Interesse Comunitário Moura/Barrancos".

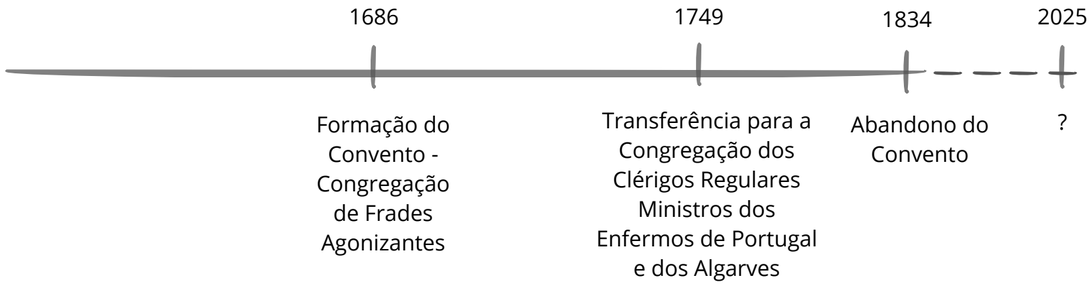

Estado avançado de ruína. Clima árido, solo xistoso, ribeiras sazonais e vegetação adaptada à escassez hídrica.

Ribeira de Pae Joannes - subida do nível da água, afetando a acessibilidade.

2. FUNDAÇÃO E CONSTRUÇÃO

Fixação dos Eremitas na Tomina - Isolamento físico do conjunto edificado - recolhimento e contemplação.
Ideia de “Deserto”, sinónimo de Convento.

Ponto elevado, de difícil acesso, densamente arborizado e com acesso a água.

Proibida a construção de edifícios definitivos.
Inicialmente, construção de pequenas choças e abrigos provisórios, erguidos com o apoio da população de Santo Aleixo,

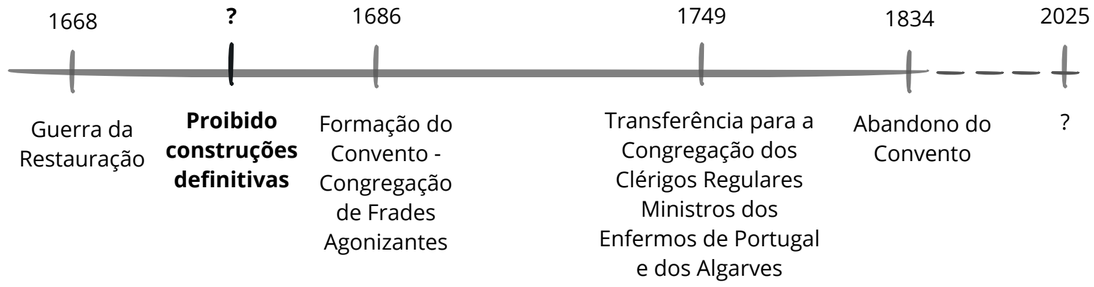

Exemplo de choça de habitação - Marvão
(Oliveira, E.V. et al, 1988)

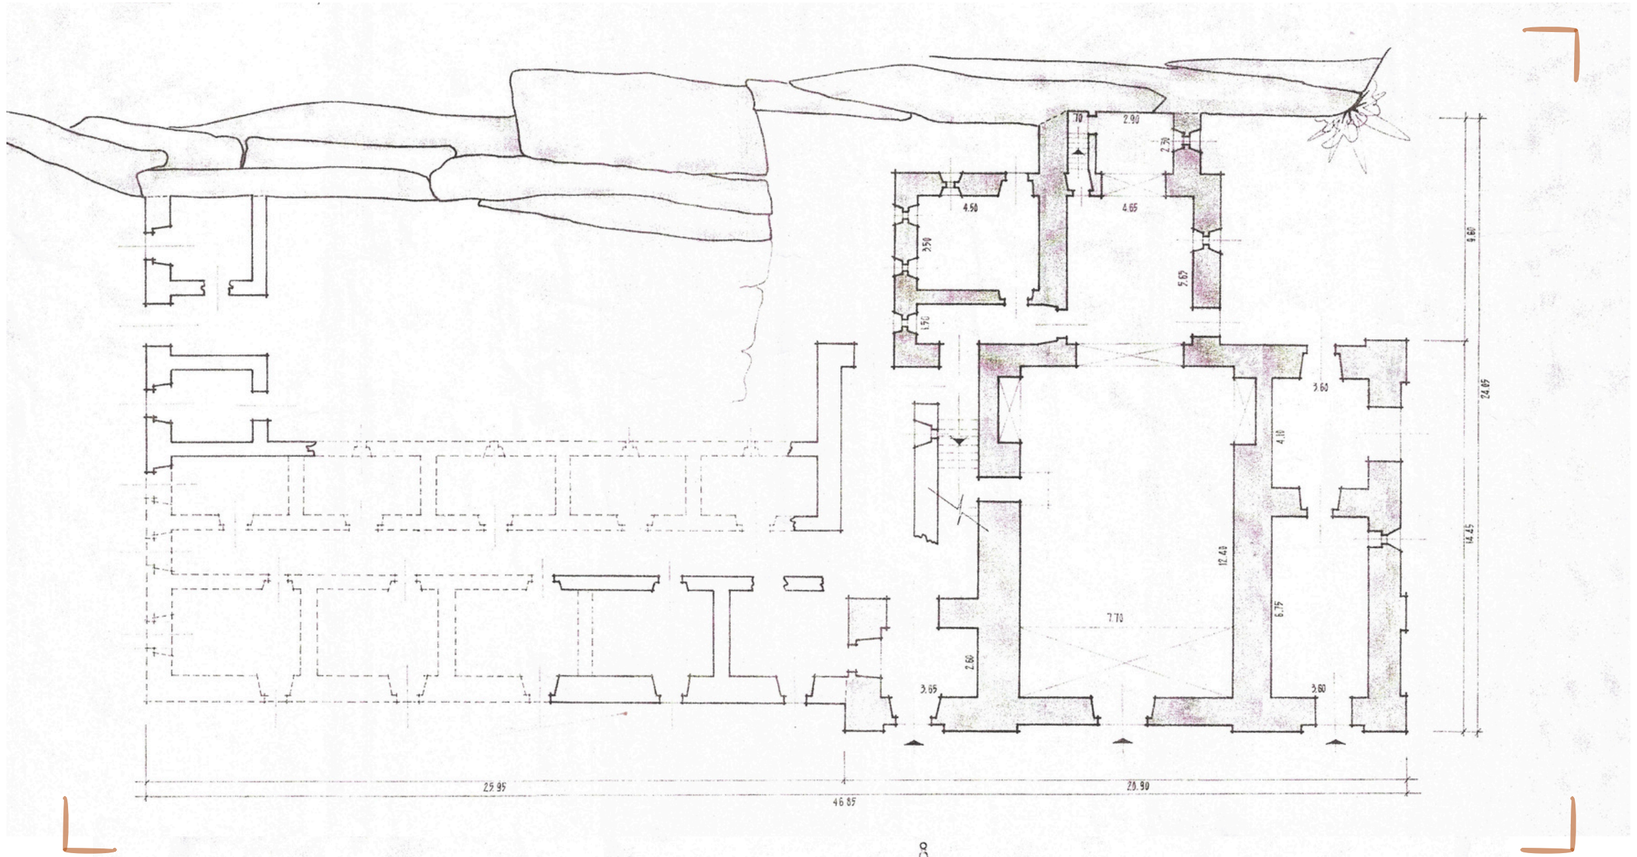

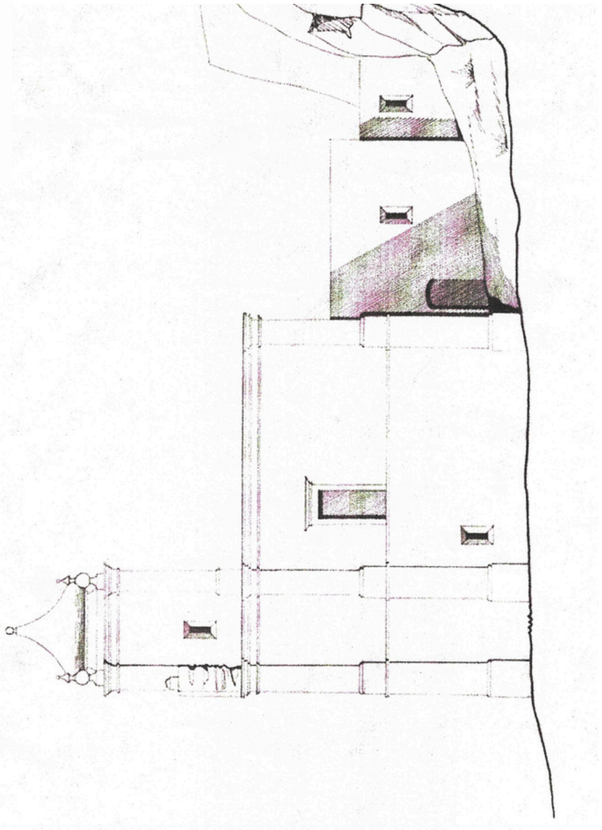

CONSTRUÇÃO EM MAU ESTADO
RUÍNAS
VESTÍGIOS DE CONSTRUÇÃO

E. 1/100
Arquivo ICNF (s/d)

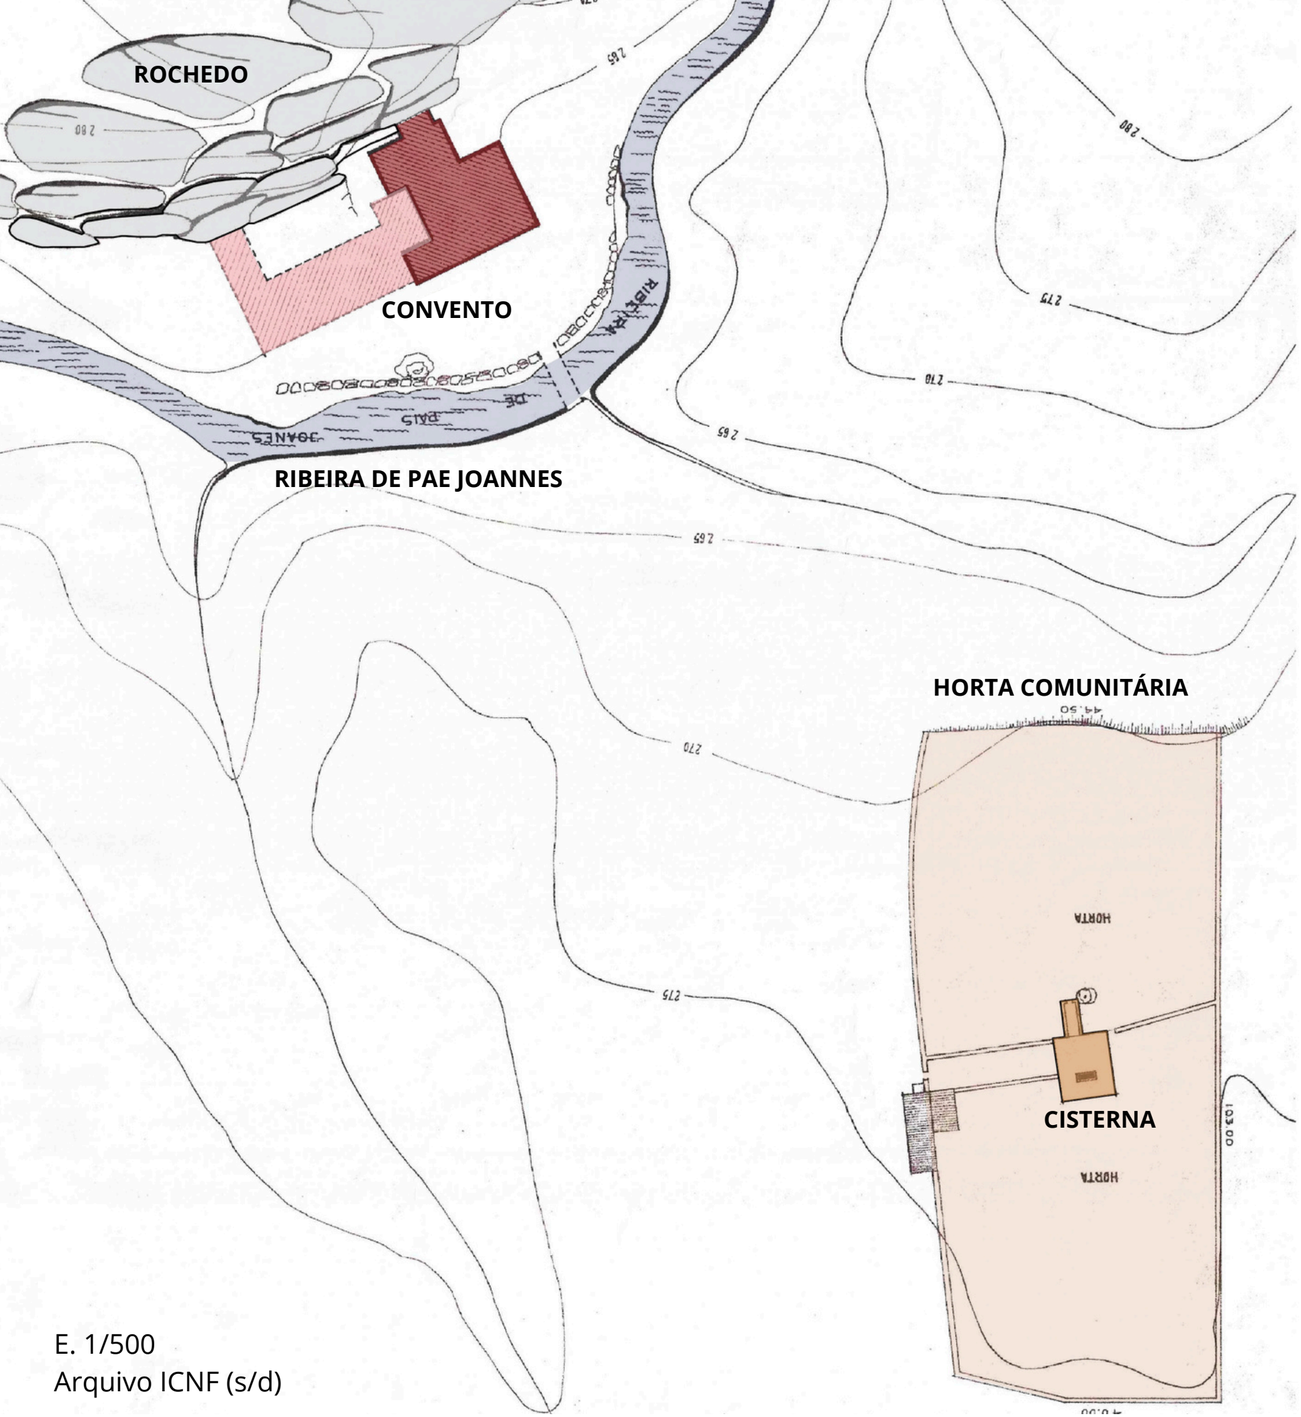

E. 1/500
Arquivo ICNF (s/d)

FUNDAÇÃO E CONSTRUÇÃO

Demolição de um grande rochedo, com ajuda dos habitantes da aldeia. Construção da Igreja (três capelas), celas, refeitório, sala de estudo, e oficinas.

1688 - Incêndio extinguido por uma chuva súbita, fenómeno atribuído à proteção da padroeira, deu origem à festa anual.

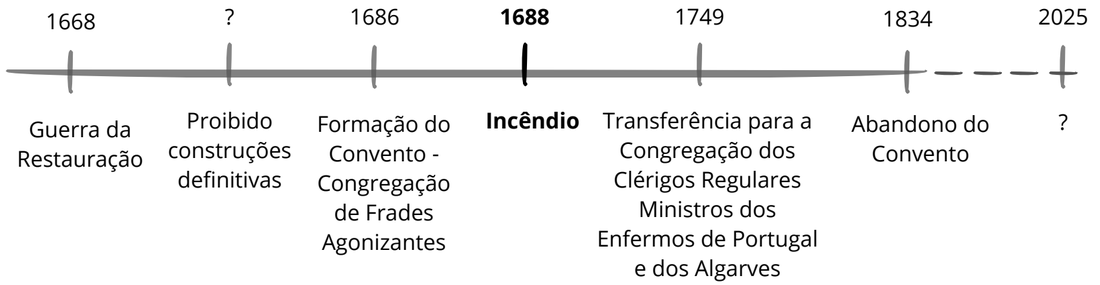

3.“ESPÍRITO DO LUGAR”

Relação entre a Arquitetura, os objetos e os lugares criados pelo Homem - “**Espírito do Luga**r” (Norberg-Schulz, 1976).

Elementos tangíveis — edifícios, paisagens, objetos.
Elementos intangíveis — memórias, rituais, festas, cores, odores e narrativas - Declaração de Quebec (ICOMOS, 2008).

RUINA
PAISAGEM
TRADIÇÕES
] Continuidade do seu valor identitário

4. CONSIDERAÇÕES FINAIS

Comunidades envolvidas no processo de preservação.

Crescente interesse pelas tradições.

Satisfazer as necessidades do presente, sem comprometer a capacidade das próximas gerações satisfazerem as suas (Brunland, 1987).

Sustentabilidade Sócio-cultural

Património Arquitetónico
Património Paisagístico
Património Cultural

Cruzamento de espaço fisico e memórias a ele associadas

Identidade de um lugar

Evitar a perda definitica deste Património tão valorizado pela comunidade local.

LABORATÓRIO COLABORATIVO: Dinâmicas Urbanas, Património, Artes
XI Seminário de Investigação, Ensino e Difusão

28 e 29 de agosto de 2025, Centro Histórico e Cultural do Mackenzie

CONVENTO DA TOMINA: CONTRIBUTOS PARA A COMPREENSÃO DA SUA IDENTIDADE PATRIMONIAL

CARLOTA ROCHA E SOFIA ALEIXO
Dep. Arquitetura – EAartes – Universidade de Évora

Mackenzie
UNIVERSIDADE DE ÉVORA
iscte INSTITUTO UNIVERSITÁRIO DE LISBOA
15 ANOS 2010-2025